GOVERNMENT OF DUBAI

LAND DEMARCATION CERTIFICATE

سلطة دبي للتطوير
Dubai Development Authority

PLOT NUMBER	6832537	PLOT AREA M²	1228.12

PLOT COORDINATES (C.S: DLTM), NOTE: ADDITIONAL ATTACHMENT FOR FULL LIST OF COORDINATE

POINT ID	POINT X	POINT Y	POINT ID	POINT X	POINT Y
1	489843.045	2768005.244	9	489805.057	2768008.659
2	489817.564	2767988.709	10	489803.510	2768011.229
3	489815.639	2767991.688	11	489801.974	2768013.806
4	489814.022	2767994.215	12	489799.108	2768018.678
5	489812.416	2767996.749	13	489797.603	2768021.273
6	489810.820	2767999.289	14	489796.108	2768023.874
7	489809.234	2768001.836	15	489821.953	2768039.505
8	489807.659	2768004.389	16	489824.791	2768034.416

LOCATION MAP

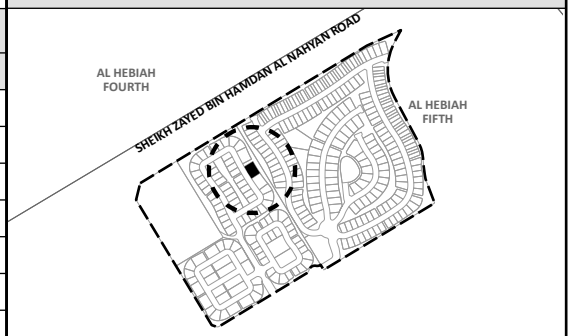

COMMUNITY	AL HEBIAH FIFTH

APPROVED

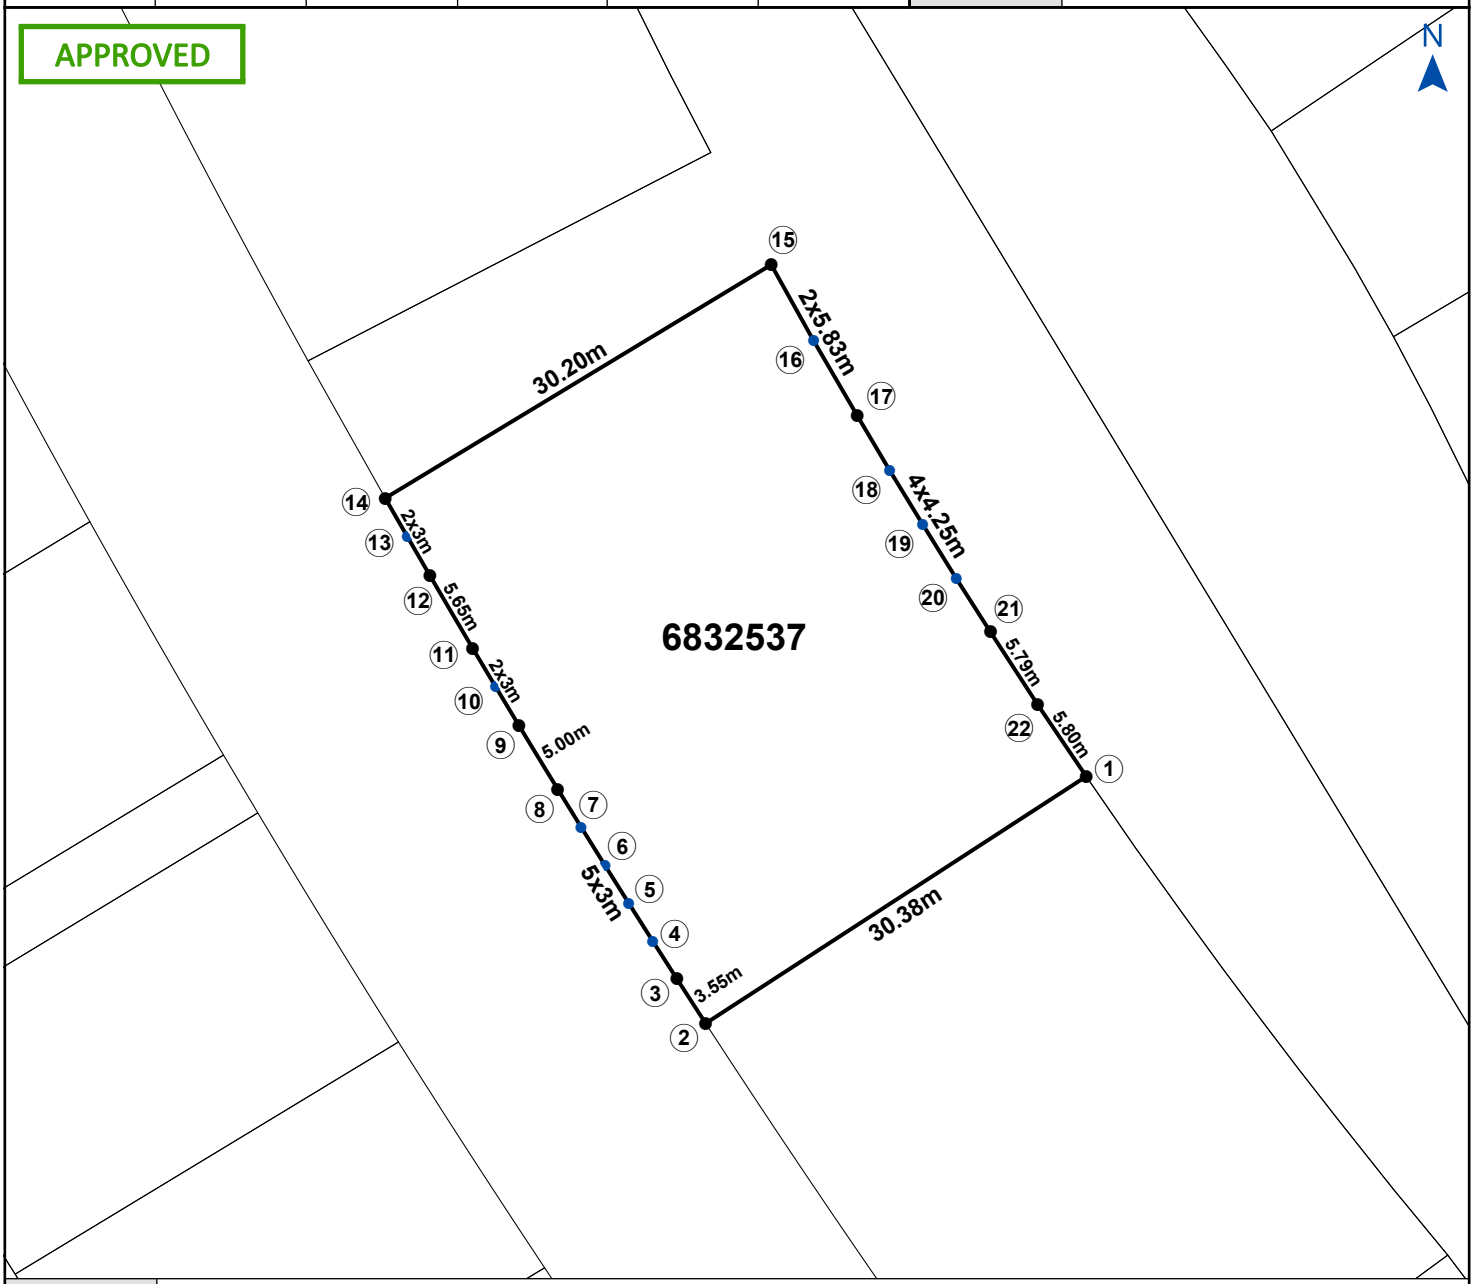

NOTES	1- THE CONTRACTOR IS FULLY LIABLE FOR ANY DEVIATION IN THE PLOT LIMIT. 2- DEMARCATION ISSUED FOR THE CONTRACTOR TO START EXCAVATION, SHORING, AND PILING. 3- THE NEXT RE-DEMARCATION REQUIRED FOR BOUNDARY WALL FOUNDATION INSPECTION.

DUBAI GOLF CITY

PROJECT NAME	DUBAI GOLF CITY
MASTER DEVELOPER	DUBAI GOLF CITY (L.L.C)

ELECTRONICALLY GENERATED DOCUMENT

DEMARCATION ID	DEMARCATED BY	ISSUE DATE
202206270002	MOHAMMAD KHALEEL	27/06/2022

PLOT NUMBER		6832537			DEMARCATION ID		202206270002	
PLOT COORDINATES (C.S: DLTM)								
POINT ID	POINT X	POINT Y	POINT ID	POINT X	POINT Y	POINT ID	POINT X	POINT Y
1	489843.045	2768005.244						
2	489817.564	2767988.709						
3	489815.639	2767991.688						
4	489814.022	2767994.215						
5	489812.416	2767996.749						
6	489810.820	2767999.289						
7	489809.234	2768001.836						
8	489807.659	2768004.389						
9	489805.057	2768008.659						
10	489803.510	2768011.229						
11	489801.974	2768013.806						
12	489799.108	2768018.678						
13	489797.603	2768021.273						
14	489796.108	2768023.874						
15	489821.953	2768039.505						
16	489824.791	2768034.416						
17	489827.724	2768029.380						
18	489829.890	2768025.723						
19	489832.108	2768022.098						
20	489834.350	2768018.485						
21	489836.638	2768014.904						
22	489839.796	2768010.047						