GOVERNMENT OF DUBAI

LAND DEMARCATION CERTIFICATE

سلطة دبي للتطوير
Dubai Development Authority

PLOT NUMBER	6832538	PLOT AREA M²	1276.04

PLOT COORDINATES (C.S: DLTM), NOTE: ADDITIONAL ATTACHMENT FOR FULL LIST OF COORDINATE

POINT ID	POINT X	POINT Y	POINT ID	POINT X	POINT Y
1	489867.250	2767973.194	9	489829.285	2767971.229
2	489841.420	2767954.212	10	489826.173	2767975.764
3	489839.412	2767956.957	11	489824.185	2767978.701
4	489837.651	2767959.387	12	489822.514	2767981.193
5	489835.901	2767961.823	13	489820.854	2767983.692
6	489834.161	2767964.267	14	489819.204	2767986.197
7	489832.718	2767966.308	15	489817.564	2767988.709
8	489830.996	2767968.765	16	489843.045	2768005.244

LOCATION MAP

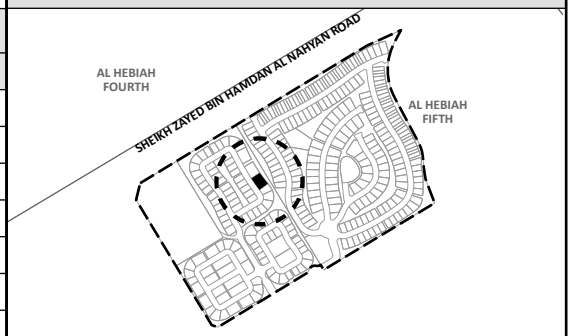

COMMUNITY	AL HEBIAH FIFTH

APPROVED

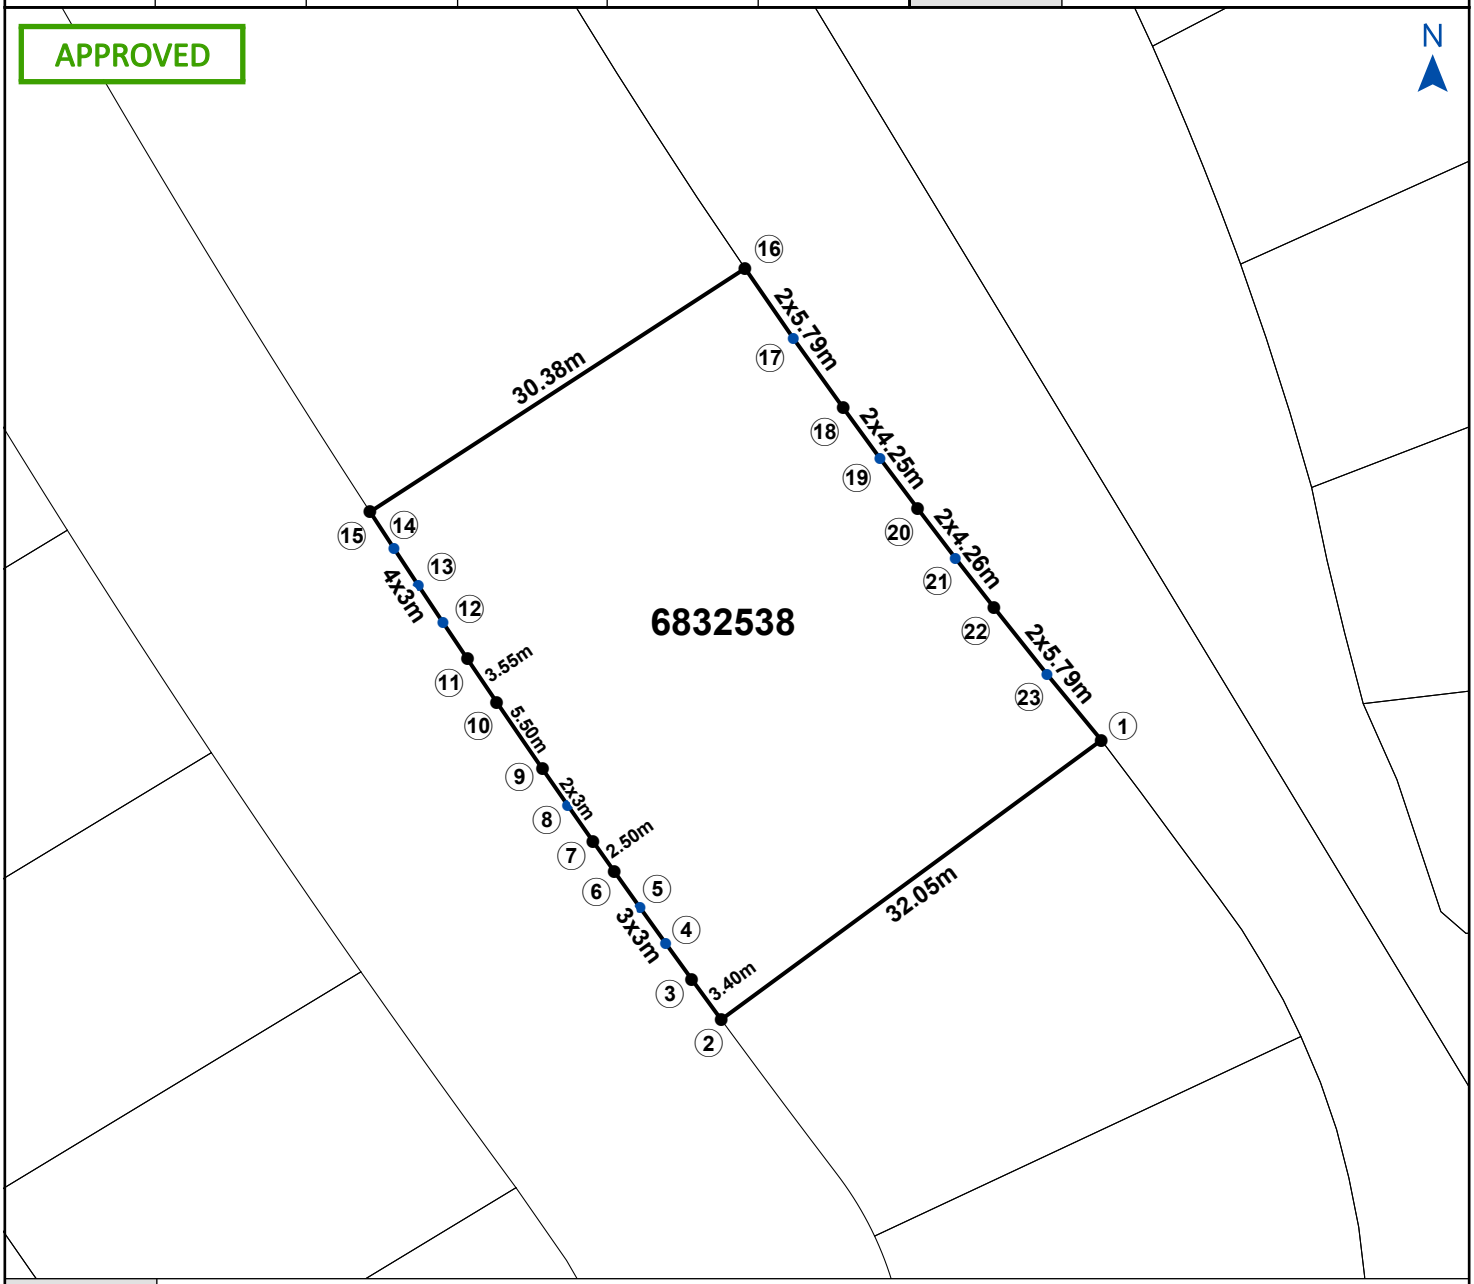

NOTES	1- THE CONTRACTOR IS FULLY LIABLE FOR ANY DEVIATION IN THE PLOT LIMIT. 2- DEMARCATION ISSUED FOR THE CONTRACTOR TO START EXCAVATION, SHORING, AND PILING. 3- THE NEXT RE-DEMARCATION REQUIRED FOR BOUNDARY WALL FOUNDATION INSPECTION.

DUBAI GOLF CITY

PROJECT NAME	DUBAI GOLF CITY
MASTER DEVELOPER	DUBAI GOLF CITY (L.L.C)

ELECTRONICALLY GENERATED DOCUMENT

DEMARCATION ID	DEMARCATED BY	ISSUE DATE
202206270003	MOHAMMAD KHALEEL	27/06/2022

COORDINATES ATTACHMENT

PLOT NUMBER		6832538			DEMARCATION ID		202206270003	
PLOT COORDINATES (C.S: DLTM)								
POINT ID	POINT X	POINT Y	POINT ID	POINT X	POINT Y	POINT ID	POINT X	POINT Y
1	489867.250	2767973.194						
2	489841.420	2767954.212						
3	489839.412	2767956.957						
4	489837.651	2767959.387						
5	489835.901	2767961.823						
6	489834.161	2767964.267						
7	489832.718	2767966.308						
8	489830.996	2767968.765						
9	489829.285	2767971.229						
10	489826.173	2767975.764						
11	489824.185	2767978.701						
12	489822.514	2767981.193						
13	489820.854	2767983.692						
14	489819.204	2767986.197						
15	489817.564	2767988.709						
16	489843.045	2768005.244						
17	489846.333	2768000.477						
18	489849.709	2767995.772						
19	489852.213	2767992.335						
20	489854.765	2767988.935						
21	489857.341	2767985.548						
22	489859.962	2767982.195						
23	489863.565	2767977.662						