GOVERNMENT OF DUBAI

LAND DEMARCATION CERTIFICATE

سلطة دبي للتطوير
Dubai Development Authority

PLOT NUMBER	6833286	PLOT AREA M²	742.61

PLOT COORDINATES (C.S: DLTM), NOTE: ADDITIONAL ATTACHMENT FOR FULL LIST OF COORDINATE

POINT ID	POINT X	POINT Y	POINT ID	POINT X	POINT Y
1	489782.374	2768107.010	9	489752.202	2768086.784
2	489762.983	2768082.552	10	489750.521	2768086.813
3	489761.642	2768083.537	11	489749.069	2768116.635
4	489760.167	2768084.352	12	489752.011	2768116.710
5	489758.661	2768085.079	13	489754.953	2768116.623
6	489757.094	2768085.666	14	489757.885	2768116.366
7	489755.491	2768086.157	15	489760.799	2768115.950
8	489753.854	2768086.521	16	489763.685	2768115.372

LOCATION MAP

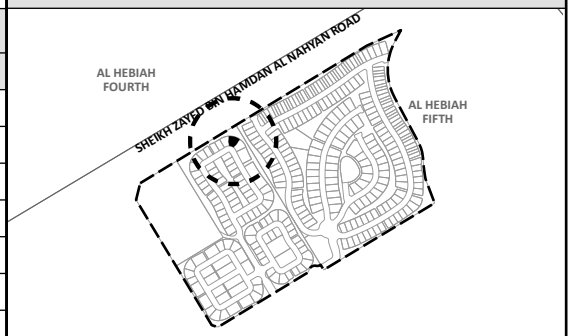

COMMUNITY	AL HEBIAH FIFTH

APPROVED

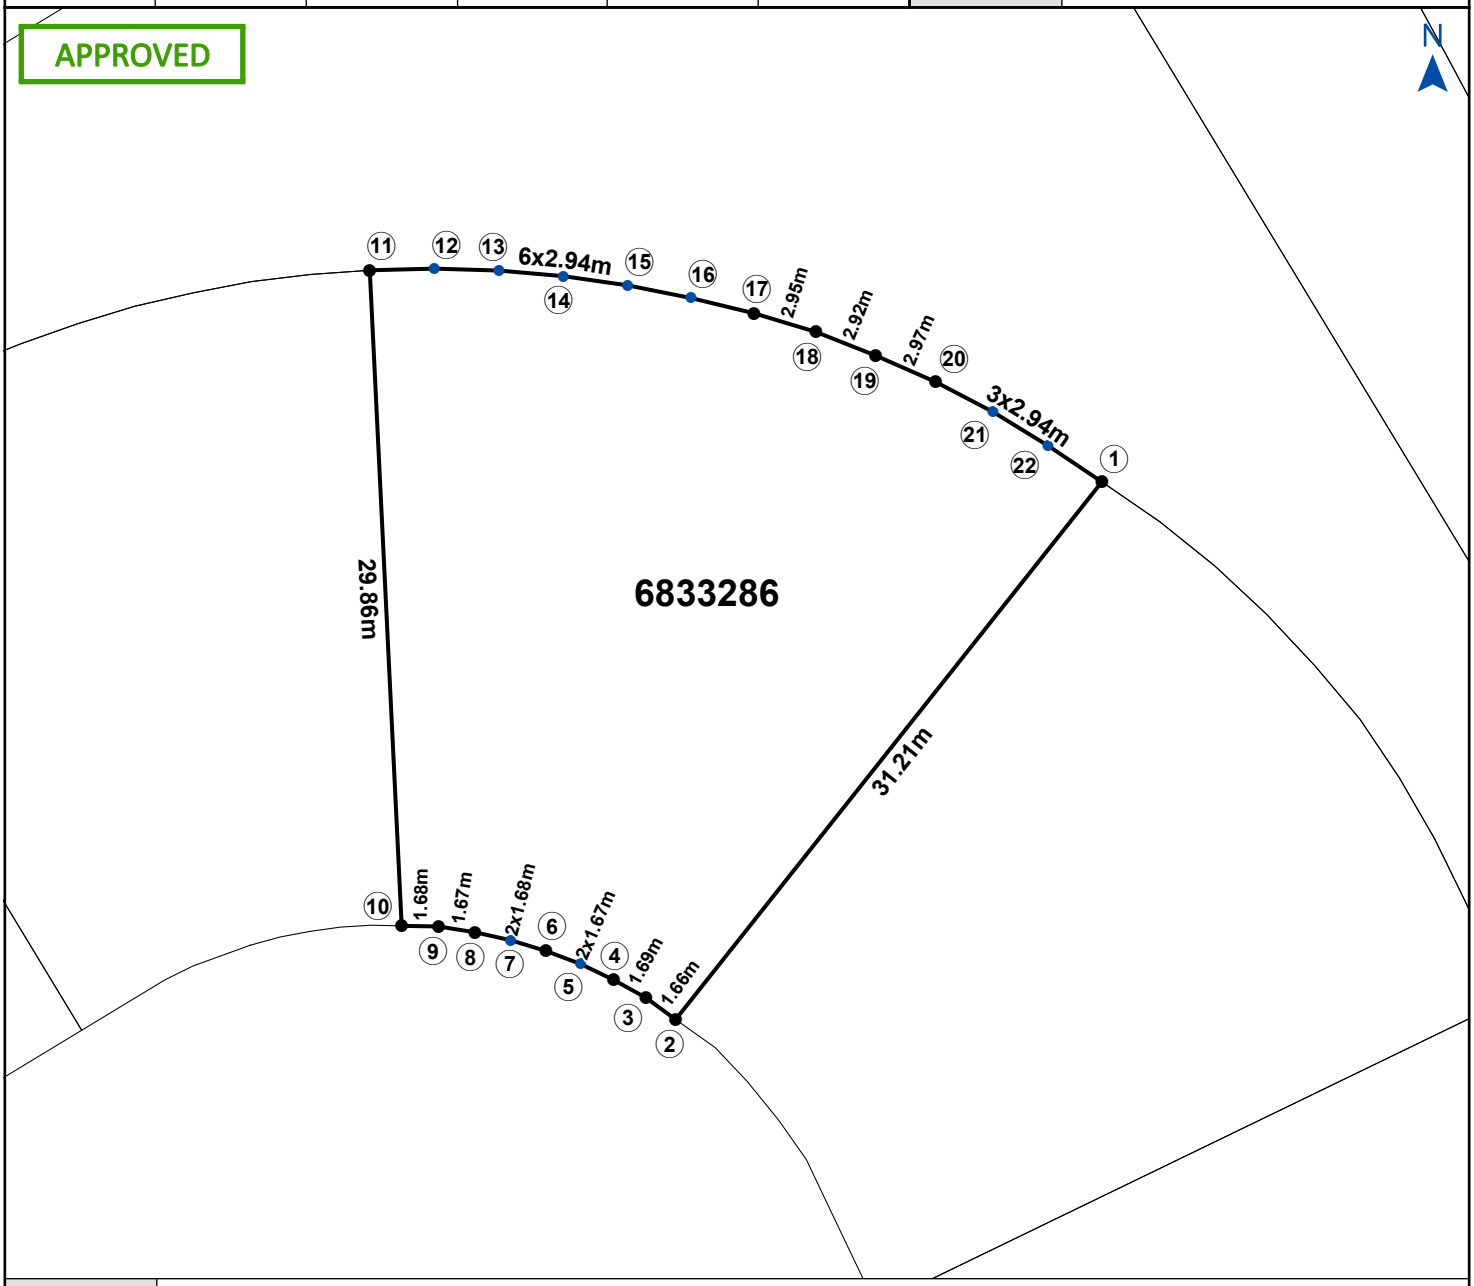

NOTES	1- THE CONTRACTOR IS FULLY LIABLE FOR ANY DEVIATION IN THE PLOT LIMIT. 2- DEMARCATION ISSUED FOR THE CONTRACTOR TO START EXCAVATION, SHORING, AND PILING. 3- THE NEXT RE-DEMARCATION REQUIRED FOR BOUNDARY WALL FOUNDATION INSPECTION.

DUBAI GOLF CITY

PROJECT NAME	DUBAI GOLF CITY
MASTER DEVELOPER	DUBAI GOLF CITY (L.L.C)

ELECTRONICALLY GENERATED DOCUMENT

DEMARCATION ID	DEMARCATED BY	ISSUE DATE
202206270004	MOHAMMAD KHALEEL	27/06/2022

COORDINATES ATTACHMENT

PLOT NUMBER		6833286			DEMARCATION ID		202206270004	
PLOT COORDINATES (C.S: DLTM)								
POINT ID	POINT X	POINT Y	POINT ID	POINT X	POINT Y	POINT ID	POINT X	POINT Y
1	489782.374	2768107.010						
2	489762.983	2768082.552						
3	489761.642	2768083.537						
4	489760.167	2768084.352						
5	489758.661	2768085.079						
6	489757.094	2768085.666						
7	489755.491	2768086.157						
8	489753.854	2768086.521						
9	489752.202	2768086.784						
10	489750.521	2768086.813						
11	489749.069	2768116.635						
12	489752.011	2768116.710						
13	489754.953	2768116.623						
14	489757.885	2768116.366						
15	489760.799	2768115.950						
16	489763.685	2768115.372						
17	489766.546	2768114.680						
18	489769.375	2768113.828						
19	489772.091	2768112.752						
20	489774.814	2768111.555						
21	489777.424	2768110.191						
22	489779.931	2768108.652						